RIVERSIDE APARTMENT 3B

Reference drawing set - not for construction

Angled facade, 45° corner, curved bay

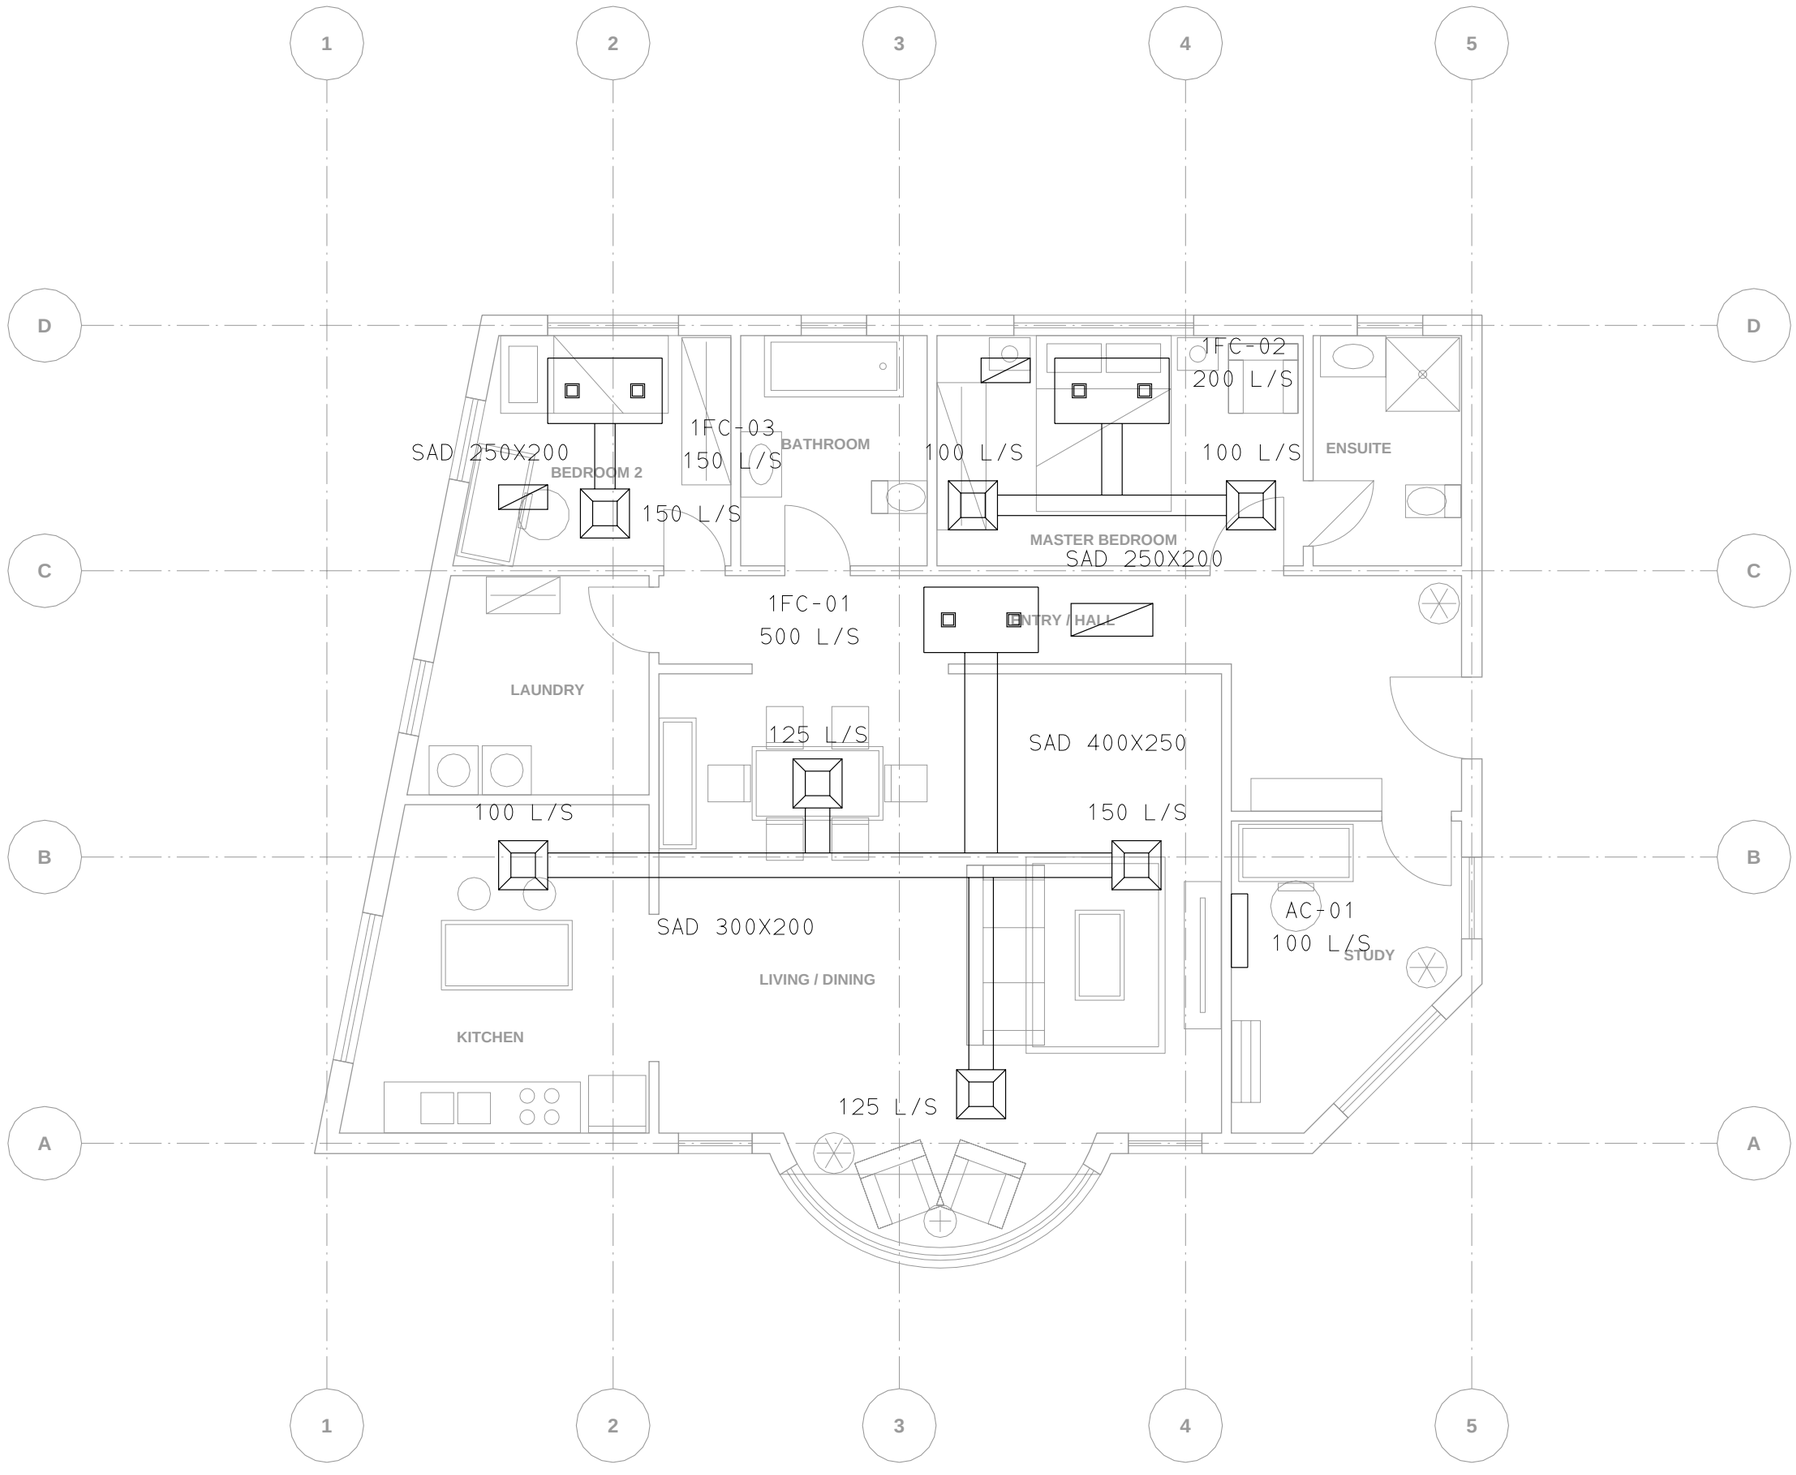

3 ducted fan coil units (1FC-01..03) in the ceiling void, 1 wall split (AC-01) in the study
Design airflows in L/s; ducts W x H in mm
Return air via ceiling grilles to the plenum
Grids as architectural drawing A-101

N

Supply air diffuser (airflow in L/s)

Return air grille

Supply air duct, size W x H mm (SAD)

1FC-xx ducted fan coil unit in the ceiling void

AC-xx wall-mounted split unit (2.2 m)

0 1 5 m

ACMV LAYOUT

LEVEL 1 (single floor)

SCALE 1:75 @ A3

Dimensions in millimetres; grid 1-5 / A-D

DRAWING M-101

REV A 2026-10-15